
DO N° 151-128-2026	Situation Géographique ZCh1	selon bordereau d'organisation	Annexe A2
Procédé S9	**ZEP OG7479**		
ZCh	**ZCh 1 : Travaux LFRP** **CCh 1 : Jessy QUATREVAUX : 06.69.02.63.43** **V1L: du Pk 24+700 au Pk 29+900** **V2L : du Pk 24+700 au Pk 29+800**		
Outils de Bouclage	**DSh sur z207 - Pk 24+700 - Voie 1L** **DSh sur z350 - Pk 29+800 - Voie 2L**		

Paris **Province**

Act 1: TX CAT : du PK 26+500 au 29+800 V1L/V2L

Act 2 : TX voie : pose de JIC du PK 24+700 AU 29+800 V1L/V2L

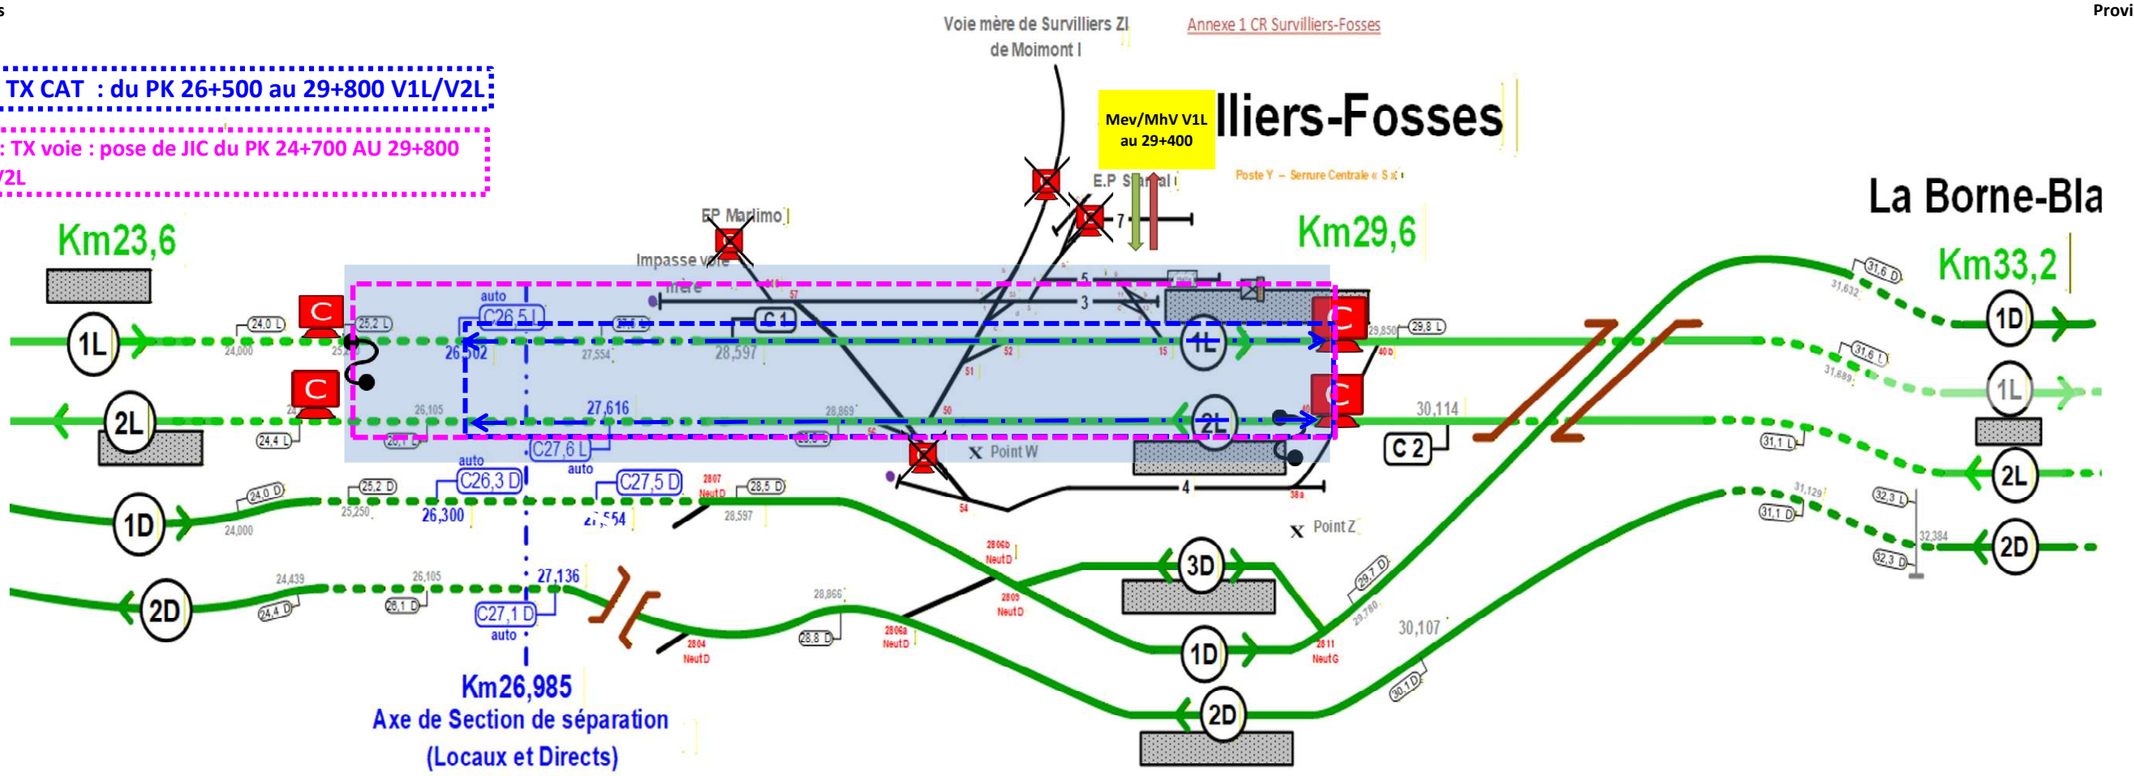


LAM / TTX	Mise en en voie	Zone d'action des LAM et/ou TTx	Mise hors voie
2 ELAN + 1 VCP + 1 Nacelle C14 + 1 pelle RR	KM 29+400 V1L		KM 29+400 V1L

LEGENDE :

- SAM de chantier appuyé d'un pétard
- SAM de Dégagement appuyé d'un pétard
- SAM de Repérage
- Dispense de SAM de chantier
- Dispositif de Shuntage DSH
- Commutateur de ZEP
- 3 Pétards
- MEV/MHV des LAM
- Jalon d'arret
- D — Dégagement TTx
- E — Engagement TTx

Contrat N°:	151/036/2026	Situation Géographique Zch1	selon bordereau d'organisation	Annexe A1
Procédé S9	ZEP Type L OG7808			
ZCh	Voie 1D : Du PK 24+700 au 29+800 Voie 2D : Du PK 24+700 au 31+129 Cch 1: Jessy QUATREVAUX 06 69 02 63 43			
Outils de Bouclage	DDSh sur Z257 - PK 24+700 - V1D DDsh sur Z362 - PK 31+129 - V2D			

Paris **Province**

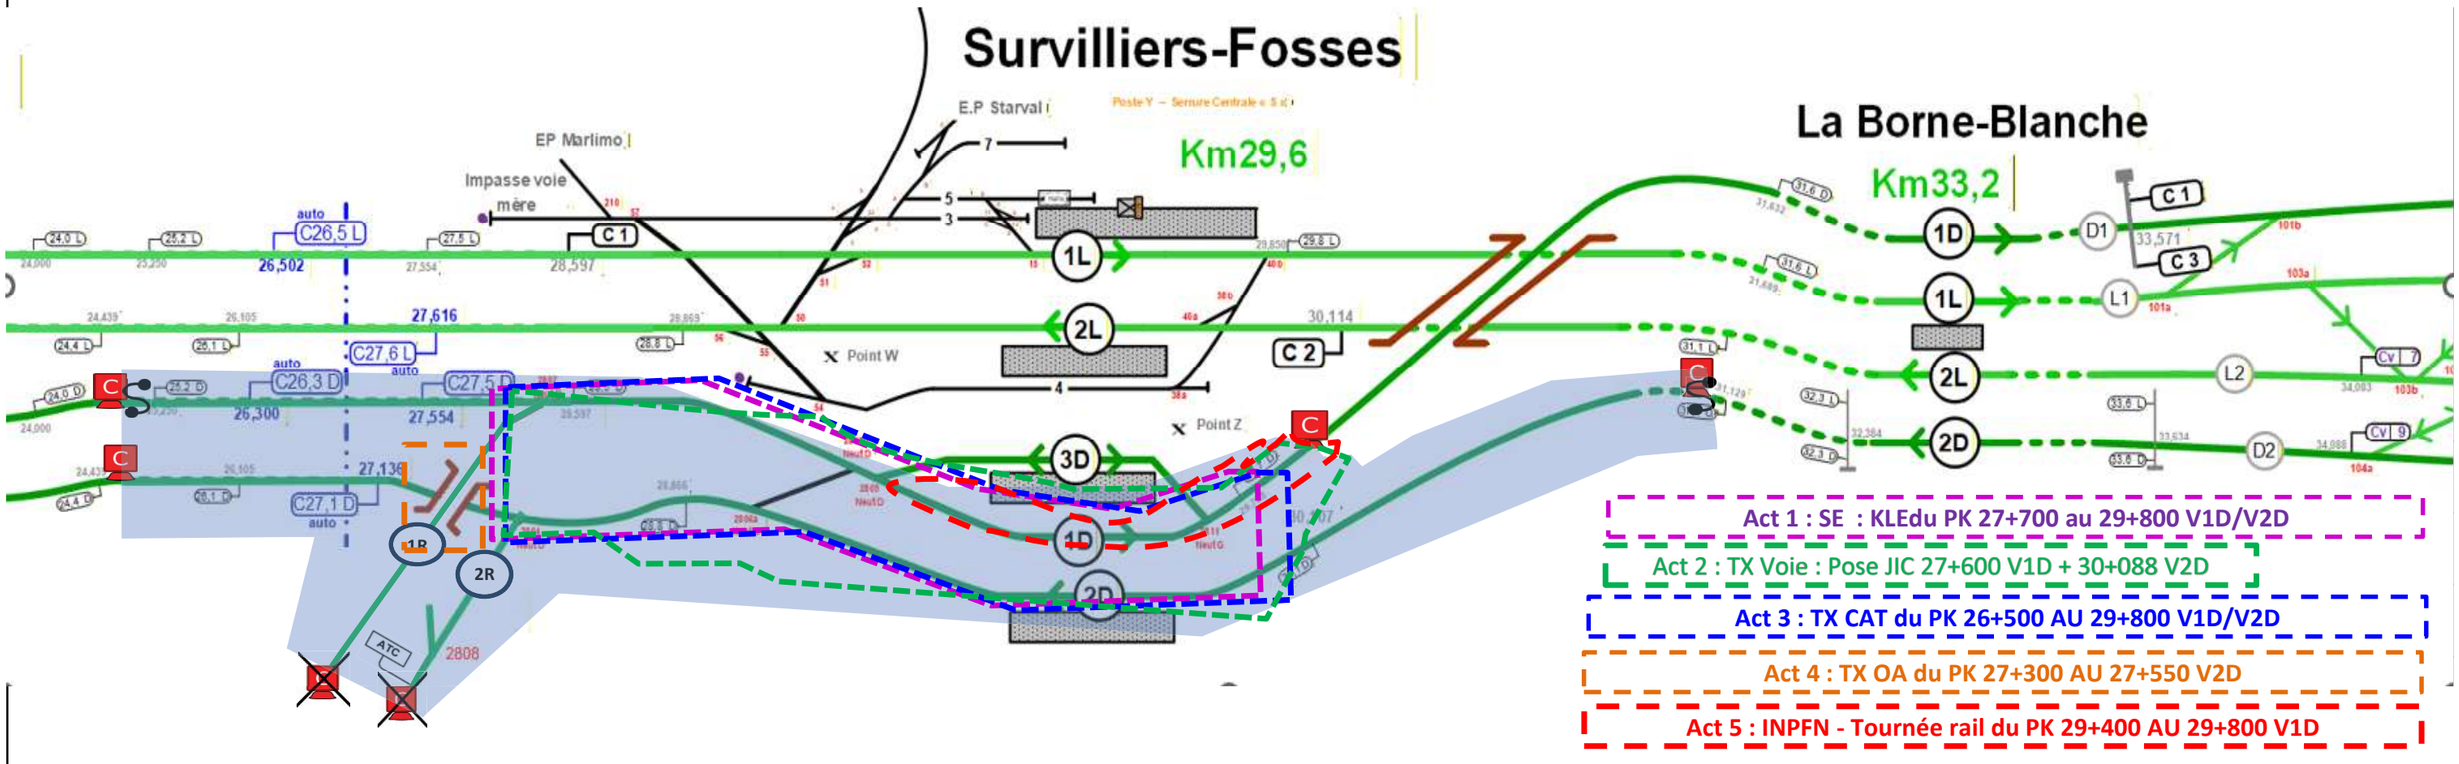


LEGENDE :

- SAM de chantier appuyé d'un pétard
- SAM de Dégagement appuyé d'un pétard
- SAM de Repérage
- Dispositif de Shuntage DSH
- Commutateur de ZEP
- 3 Pétards
- MEV/MHV des LAM
- Dispense de SAM de chantier

Contrat N°:	151/036/2026	Situation Géographique Zch02	selon bordereau d'organisation	Annexe A2
Procédé S9		ZEP Type L OG7808		
ZCh		ZCh02: Enraillement pelle RR 19+600 Du PK 19+093 au 19+650 sur V1D Du PK 19+252 au 19+650 sur V2D		
Outils de Bouclage		Voie 1D : DDSh : Sur Zone z153 - PK 19+093 Voie 2D : DDSh : Sur Zone z146 - PK 19+650		

Paris

Province

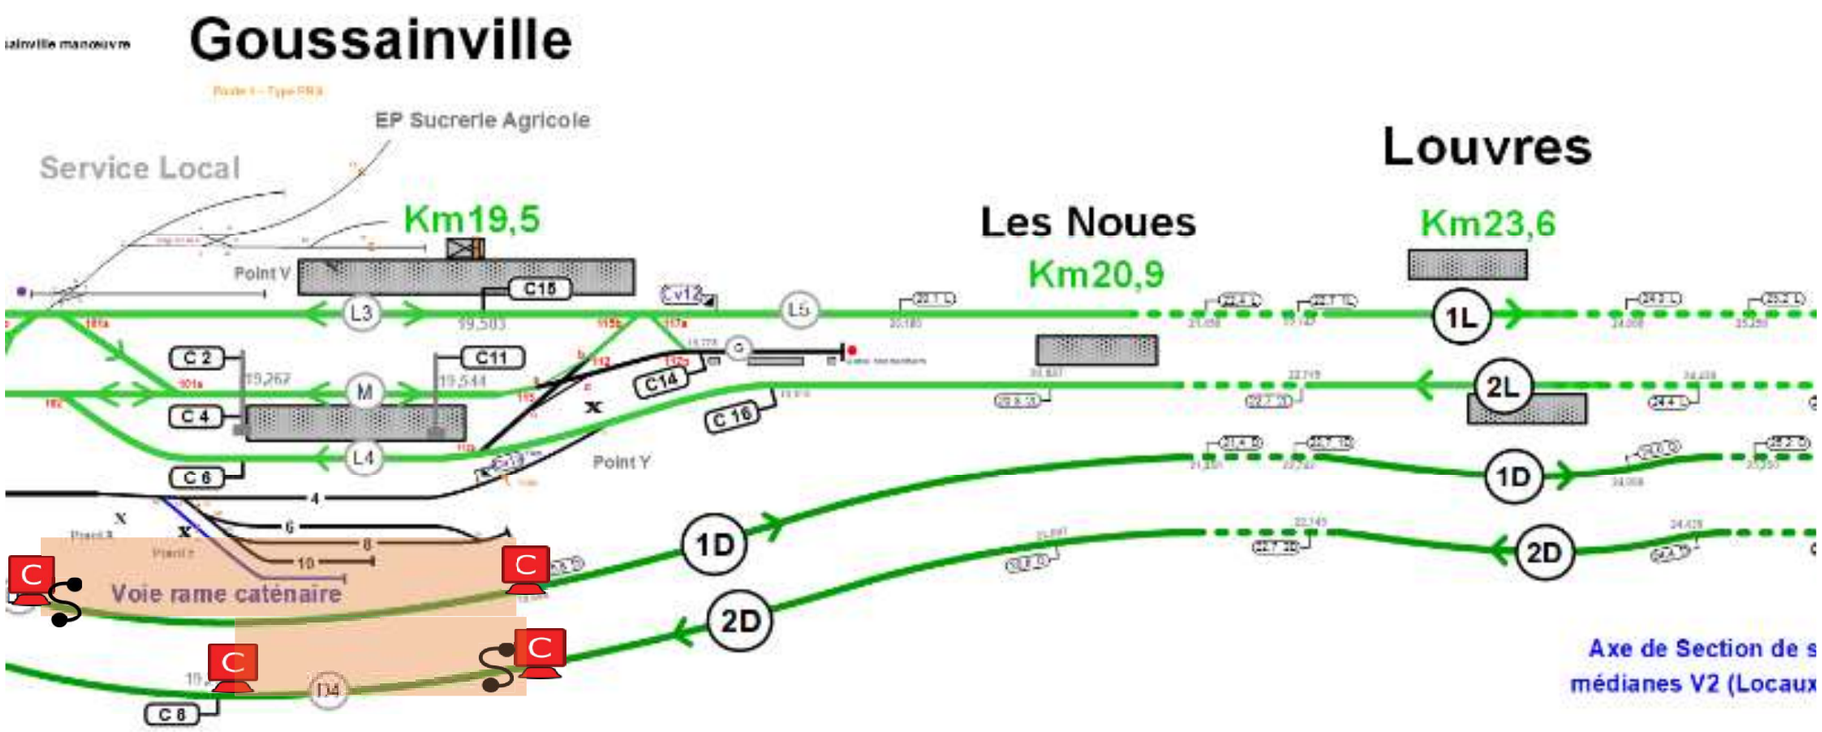


LEGENDE :					
	SAM de chantier appuyé d'un pétard		Dispositif de Shuntage DSH		3 Pétards
	SAM de Dégagement appuyé d'un pétard				
	SAM de Repérage		Commutateur de ZEP		MEV/MHV des LAM

Contrat N°:	151/036/2026	Situation Géographique LAM 1	selon bordereau d'organisation	Annexe A4

Procédé S9	**ZEP Type L OG7808**
ZCh	**Voie 1D : Du PK 24+700 au 29+800** **Voie 2D : Du PK 24+700 au 31+129** **Cch 1: Jessy QUATREVAUX 06 69 02 63 43**
Outils de Bouclage	**DDSh sur Z257 - PK 24+700 - V1D** **DDsh sur Z362 - PK 31+129 - V2D**

Paris **Province**

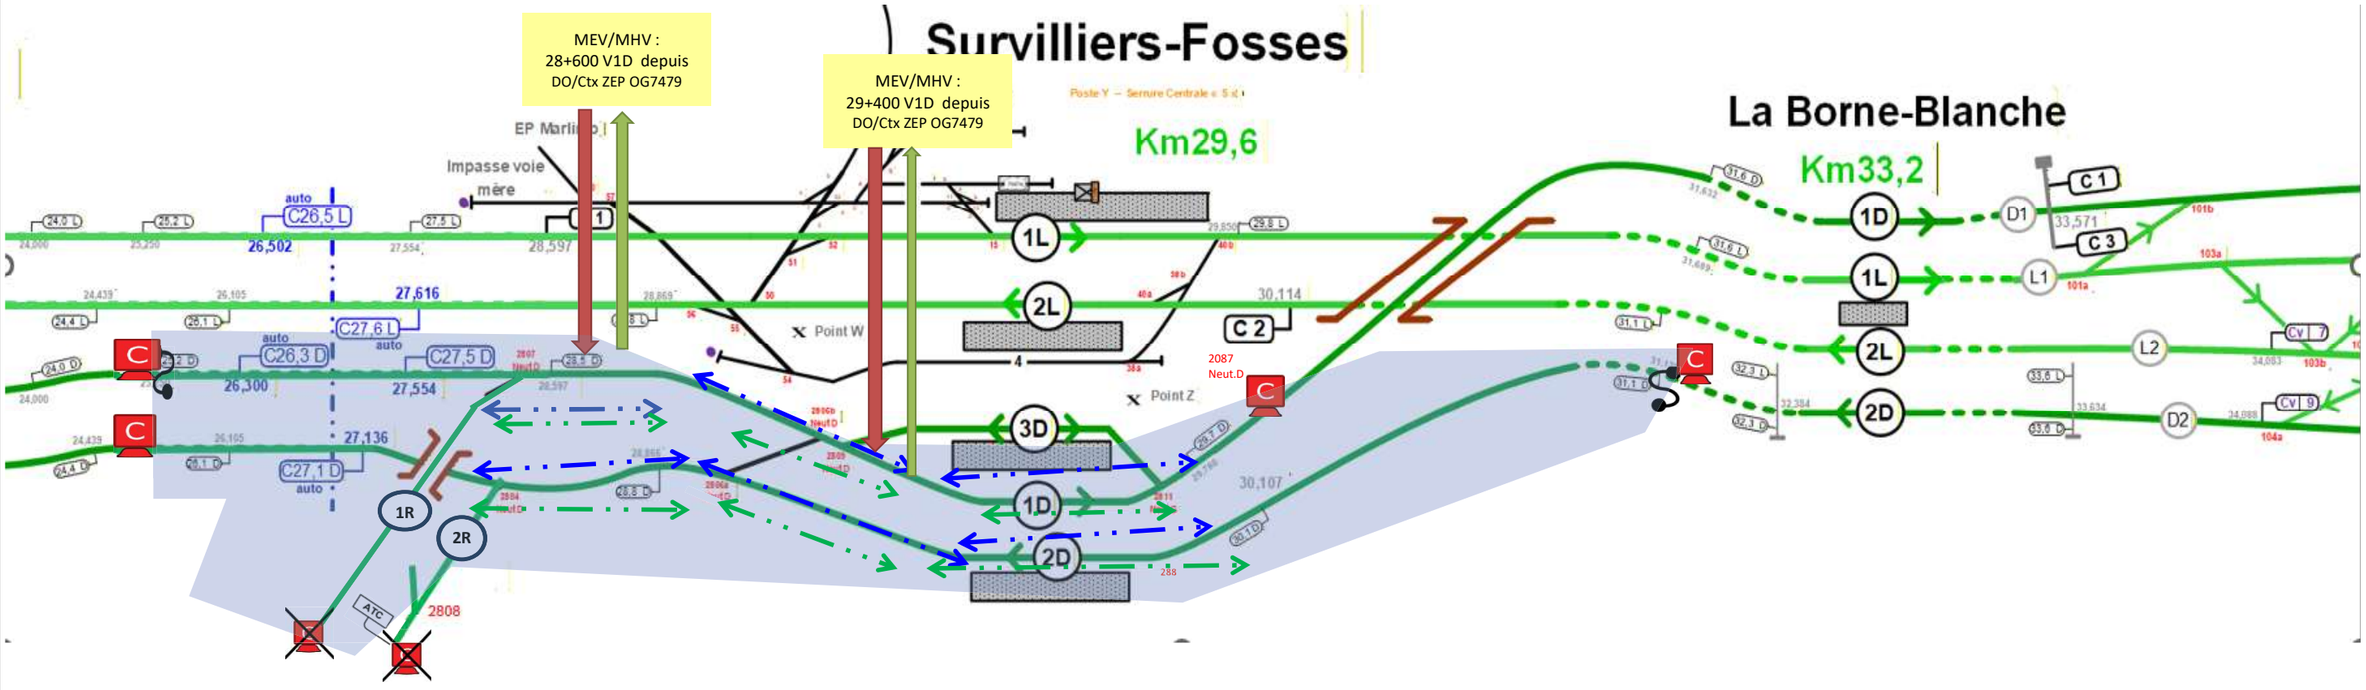

LAM / TTX	Mise en voie	Zone d'action des LAM	Mise hors voie
2 ELAN + 1 VCP + 1 NACELLE C14 +1 Pelle RR	29+400V1D depuis ZEP OG7479 (Vloc)		29+400 V1D vers ZEP OG7479 (Vloc)
1 pelle RR	28+600 V1D depuis ZEP OG7479 (Vloc)		28+600 V1D vers ZEP OG7479 (Vloc)

LEGENDE :

- C — SAM de chantier appuyé d'un pétard
- C — SAM de Dégagement appuyé d'un pétard
- R — SAM de Repérage
- Dispositif de Shuntage DSH
- Commutateur de ZEP
- 3 Pétards
- MEV/MHV des LAM
- Jalon d'arret
- D — Dégagement TTx
- E — Engagement TTx
- Dispense de SAM de chantier